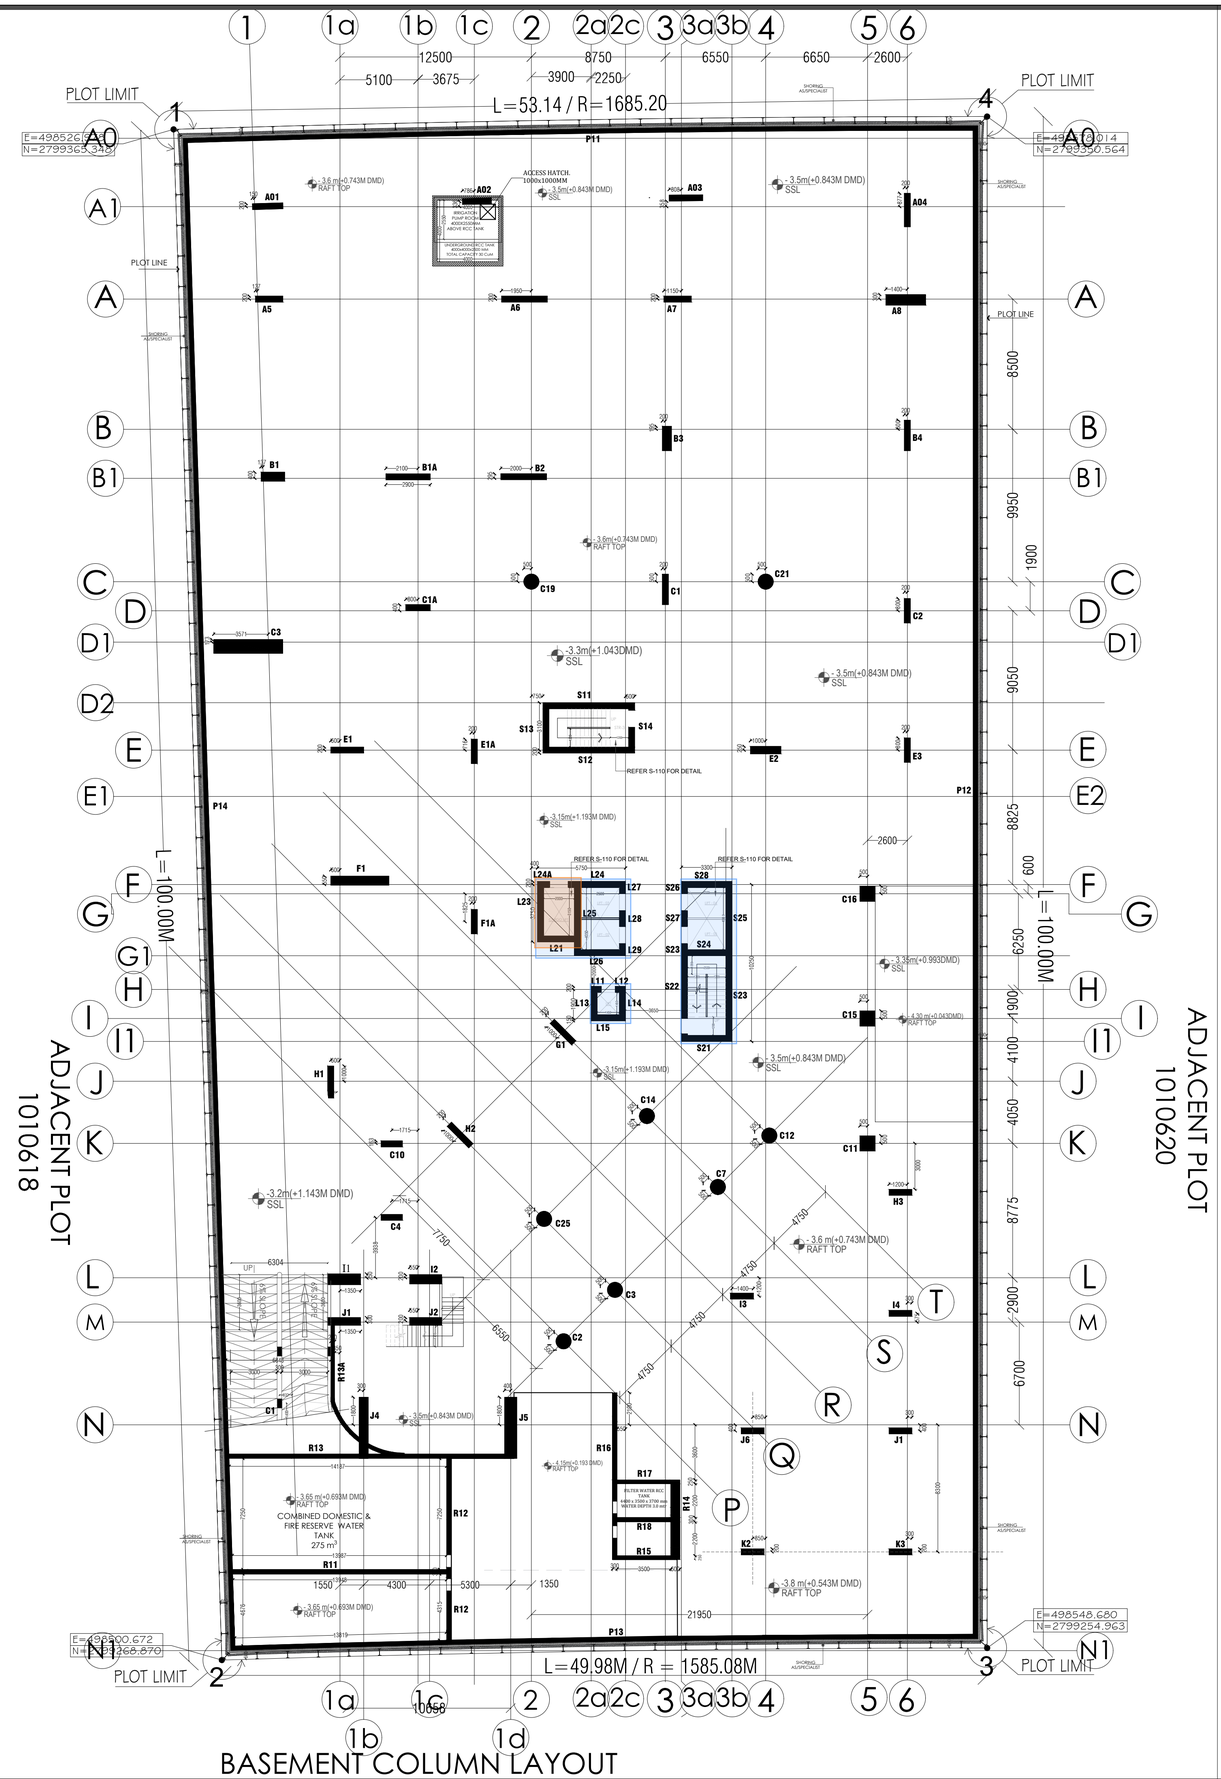


CIVIL ENGINEERING DEPARTMENT

Drawing has been **reviewed** for compliance with the Regulations and is:

NO OBJECTION

Permit Engineer: ..... Date .....

Subject to compliance with designed codes, approved architectural and structural, EHS regulation and Dubai civil defence requirments

NOTE :

(1) THIS DRAWING IS THE PROPERTY OF :
AL SARAYA ENGINEERING CONSULTANT
P.O.BOX: 49162, DUBAI, U.A.E
IT IS NOT ALLOWED TO REPRODUCE ITS CONTENTS IN ANY FORM EXCEPT FOR THE PURPOSE FOR WHICH IT IS INTENDED.

(2) THIS DRAWING IS NOT TO BE SCALED. STATED DIMENSIONS ONLY ARE TO BE CONSIDERED. DIMENSIONS ARE IN CENTIMETERS ONLY.

(3) ANY DISCREPANCIES ARE TO BE BROUGHT TO THE ATTENTION OF THE ENGINEER AND RESOLVED BEFORE COMMENCEMENT OF ANY WORK.

NOTES:

1. fcu = 50 N/mm²
2. fy = 460 N/mm²

* ALL THE SERVICE OPENINGS TO BE COORDINATED WITH ARCHITRCTURAL AND MEP DRAWINGS.

NOTE: 34% OPC + 66% GGBS + 5% MICRO SILICA

LEGEND:

- COLUMN CONTINUED TO TOP FLOOR
- COLUMN ENDING AT FLOOR LEVEL
- FLOATING COLUMN STARTING FROM FLOOR LEVEL

السرايا
الاستشارات الهندسية
AL SARAYA
ENGINEERING CONSULTANTS
P.O.Box 49162 Dubai - U.A.E.
Tel.: 04-3350084
Fax: 04-3350087

REVISIONS:

NO.	DESCRIPTION:	DATE:
00	FOR TENDER	---
01	FOR APPROVAL	13.01.25
02	FOR BP APPROVAL	24.04.25
03	FOR BP APPROVAL	16.06.25
04		

DEVELOPER:
B M L INVESTMENT LLC

OWNER:
DUBAI ISLANDS L.L.C

DESIGNER:

CONSULTANT:
AL SARAYA ENGINEERING CONSULTANTS
السرايا للاستشارات الهندسية
Architects , Engineers , Planners P.O.Box - 49162 , DUBAI, U.A.E.
Tel 04-3350084 Fax 04-3350087 E-mail :sarayadx@emirates.net.ae

SUSTAINABLE & MEP CONSULTANT
CONSISTENT ENGINEERING CONSULTANTS
Post Box No: 125786,
Office 2001 & 2002,
AFI World Tower, Sheikh Zayed Road,
Opp. World Trade Centre, Dubai.
Tel: +971-4 3860601
Fax: +971-4 3860602
Email: info@consistentconsultants.com
Website: consistentconsultants.com

COMMUNITY: NAKHLAT DEIRA-101 | PLOT: 1010619

PROJECT:
PROPOSED B+G+7+R HOTEL
ON PLOT NO.DIA-WE-0032(1010619),
NAKHLAT DEIRA-101,DUBAI


DRG. TITLE:
BASEMENT COLUMN LAYOUT
(RAFT COLUMN LAYOUT)

SCALE:	1:150/A1	KEY:	–
APPROVED BY:	SJ	DRAWN BY:	SPP
DATE:	---	PLOTTED ON:	–
PRELIMINARY	FINAL	ADDITION	REVISION
ISSUED FOR:	–		

JOB NO. : 624

DRG. NO.: S-101

REV. 00

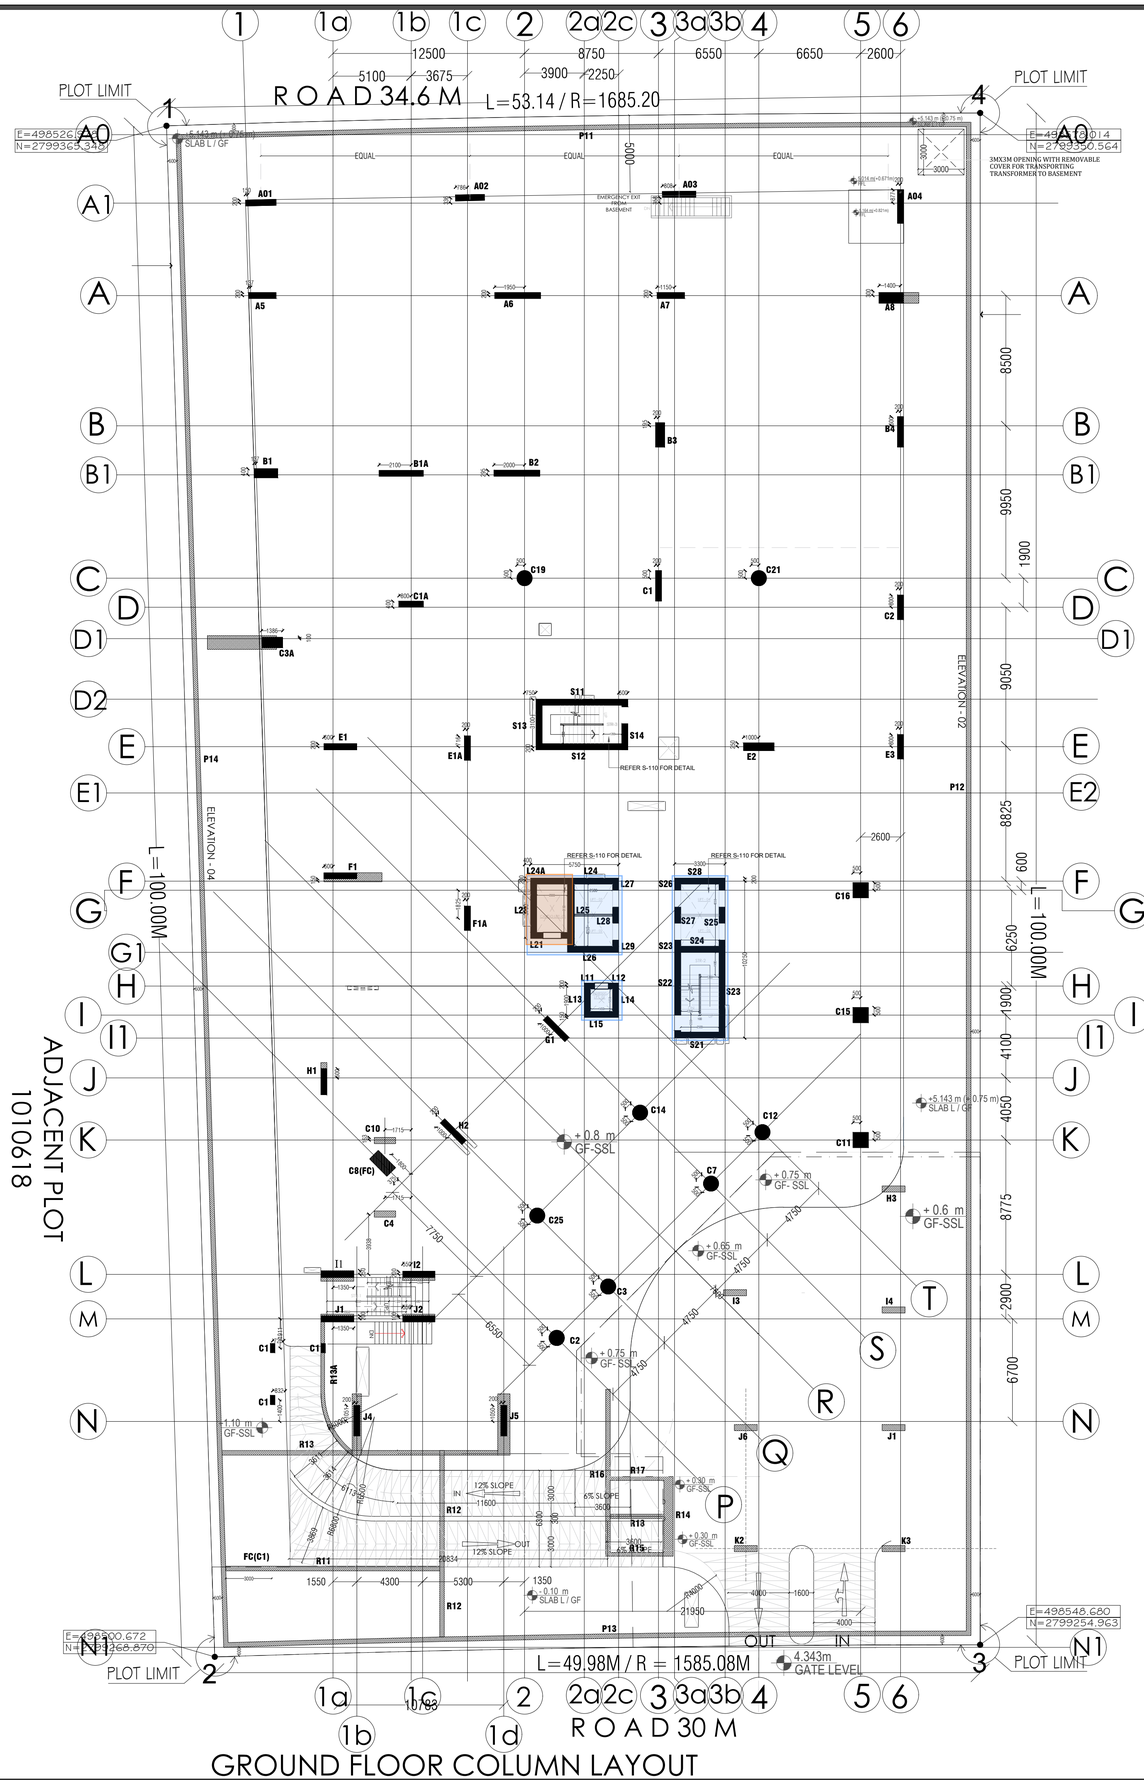

NOTE :

(1) THIS DRAWING IS THE PROPERTY OF :
AL SARAYA ENGINEERING CONSULTANT
P.O.BOX: 49162, DUBAI, U.A.E.
IT IS NOT ALLOWED TO REPRODUCE ITS CONTENTS IN ANY FORM EXCEPT FOR THE PURPOSE FOR WHICH IT IS INTENDED.

(2) THIS DRAWING IS NOT TO BE SCALED. STATED DIMENSIONS ONLY ARE TO BE CONSIDERED. DIMENSIONS ARE IN CENTIMETERS ONLY.

(3) ANY DISCREPANCIES ARE TO BE BROUGHT TO THE ATTENTION OF THE ENGINEER AND RESOLVED BEFORE COMMENCEMENT OF ANY WORK.

NOTES:

1. fcu = 50 N/mm²
2. fy = 460 N/mm²

* ALL THE SERVICE OPENINGS TO BE COORDINATED WITH ARCHITRCTURAL AND MEP DRAWINGS.

LEGEND:

- COLUMN CONTINUED TO TOP FLOOR
- COLUMN ENDING AT FLOOR LEVEL
- FLOATING COLUMN STARTING FROM FLOOR LEVEL

CIVIL ENGINEERING DEPARTMENT

Drawing has been reviewed for compliance with the Regulations and is:

NO OBJECTION

Permit Engineer: ..... Date .....

Subject to compliance with designed codes, approved architectural and structural, EHS regulation and Dubai civil defence requirments

AL SARAYA ENGINEERING CONSULTANTS
P.O.Box 49162 Dubai - U.A.E. Tel.: 04-3350084 Fax: 04-3350087

REVISIONS:

NO.	DESCRIPTION:	DATE:
00	FOR TENDER	---
01	FOR APPROVAL	13.01.25
02	FOR BP APPROVAL	24.04.25
03	FOR BP APPROVAL	16.06.25
04		

DEVELOPER:
B M L INVESTMENT LLC

OWNER:
DUBAI ISLANDS L.L.C

DESIGNER:

CONSULTANT:
AL SARAYA ENGINEERING CONSULTANTS
السرايا للإستشارات الهندسية
Architects , Engineers , Planners P.O.Box - 49162 , DUBAI, U.A.E.
Tel 04-3350084 Fax 04-3350087 E-mail :sarayada@emirates.net.ae

SUSTAINABLE & MEP CONSULTANT
CONSISTENT ENGINEERING CONSULTANTS
Post Box No: 125786, Office 2001 & 2002, API World Tower, Sheikh Zayed Road, Opp. World Trade Centre, Dubai.
Tel: +971-4 3806601
Fax: +971-4 3806602
Email: info@consistentconsultants.com
Website: consistentconsultants.com

COMMUNITY: NAKHLAT DEIRA-101 | PLOT: 1010619

PROJECT:
PROPOSED B+G+7+R HOTEL
ON PLOT NO.DIA-WE-0032(1010619),
NAKHLAT DEIRA-101,DUBAI


DRG. TITLE:
GROUND FLOOR
COLUMN LAYOUT

SCALE:	1:150/A1	KEY:	–
APPROVED BY:	SJ	DRAWN BY:	SPP
DATE:	--	PLOTTED ON:	–
PRELIMINARY	FINAL	ADDITION	REVISION
ISSUED FOR:	–		

JOB NO. : 624

DRG. NO.: S-102

REV. 00

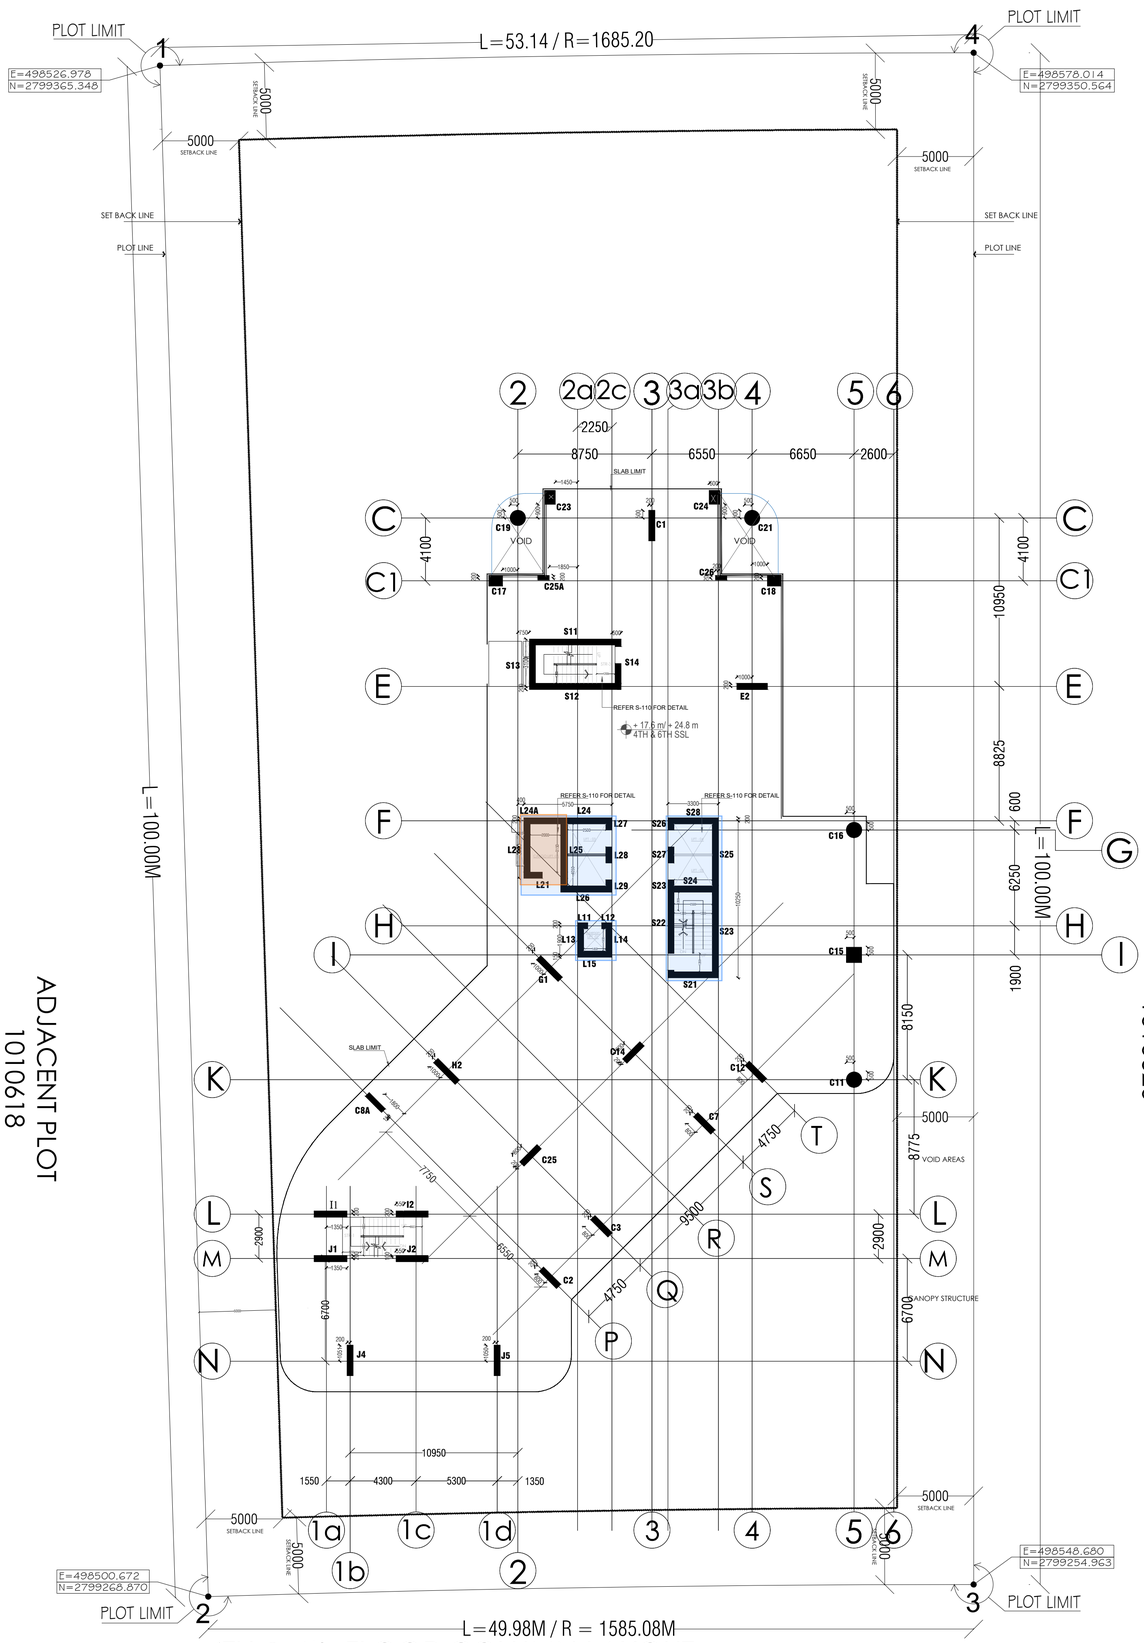

4TH & 6th FLOOR COLUMN LAYOUT

NOTE :

(1) THIS DRAWING IS THE PROPERTY OF :
AL SARAYA ENGINEERING CONSULTANT
P.O.BOX: 49162, DUBAI, U.A.E
IT IS NOT ALLOWED TO REPRODUCE ITS CONTENTS IN ANY FORM EXCEPT FOR THE PURPOSE FOR WHICH IT IS INTENDED.

(2) THIS DRAWING IS NOT TO BE SCALED. STATED DIMENSIONS ONLY ARE TO BE CONSIDERED. DIMENSIONS ARE IN CENTIMETERS ONLY.

(3) ANY DISCREPANCIES ARE TO BE BROUGHT TO THE ATTENTION OF THE ENGINEER AND RESOLVED BEFORE COMMENCEMENT OF ANY WORK.

NOTES:

1. fcu = 50 N/mm²
2. fy = 460 N/mm²

* ALL THE SERVICE OPENINGS TO BE COORDINATED WITH ARCHITRCTURAL AND MEP DRAWINGS.

LEGEND:

- COLUMN CONTINUED TO TOP FLOOR
- COLUMN ENDING AT FLOOR LEVEL
- FLOATING COLUMN STARTING FROM FLOOR LEVEL

CIVIL ENGINEERING DEPARTMENT

Drawing has been **reviewed** for compliance with the Regulations and is:

NO OBJECTION

Permit Engineer: ..... Date .....

Subject to compliance with designed codes, approved architectural and structural, EHS regulation and Dubai civil defence requirments

AL SARAYA ENGINEERING CONSULTANTS
P.O.Box 49162 Tel.: 04-3350084
Dubai - U.A.E. Fax: 04-3350087

REVISIONS:

NO.	DESCRIPTION:	DATE:
00	FOR TENDER	---
01	FOR APPROVAL	13.01.25
02	FOR BP APPROVAL	24.04.25
03	FOR BP APPROVAL	16.06.25
04		

DEVELOPER:
B M L INVESTMENT LLC

OWNER:
DUBAI ISLANDS L.L.C

DESIGNER:

CONSULTANT:
AL SARAYA ENGINEERING CONSULTANTS
السرايا للاستشارات الهندسية
Architects , Engineers , Planners P.O.Box - 49162 , DUBAI, U.A.E.
Tel 04-3350084 Fax 04-3350087 E-mail :sarayadx@emirates.net.ae

SUSTAINABLE & MEP CONSULTANT
CONSISTENT ENGINEERING CONSULTANTS
Post Box No: 125786,
Office 2001 & 2002,
API World Tower, Sheikh Zayed Road,
Opp. World Trade Centre, Dubai.
Tel: +971-4 3860601
Fax: +971-4 3860602
Email: info@consistentconsultants.com
Website: consistentconsultants.com

COMMUNITY: NAKHLAT DEIRA-101 | PLOT: 1010619

PROJECT:
PROPOSED B+G+7+R HOTEL
ON PLOT NO.DIA-WE-0032(1010619),
NAKHLAT DEIRA-101,DUBAI

DRG. TITLE:
4TH & 6TH FLOOR
COLUMN LAYOUT

SCALE:	1:150/A1	KEY:	–
APPROVED BY:	SJ	DRAWN BY:	SPP
DATE:	--	PLOTTED ON:	–


PRELIMINARY | FINAL | ADDITION | REVISION

ISSUED FOR: —


JOB NO. : 624

DRG. NO.: S-106

REV. 00

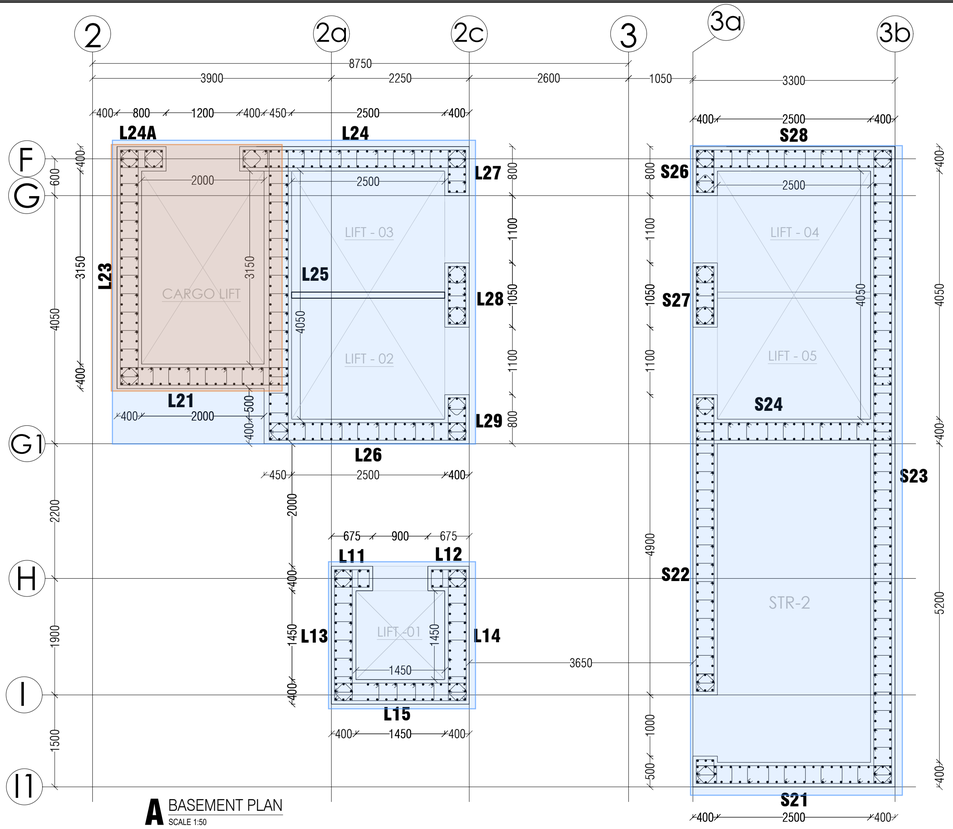


A BASEMENT PLAN
SCALE 1:50

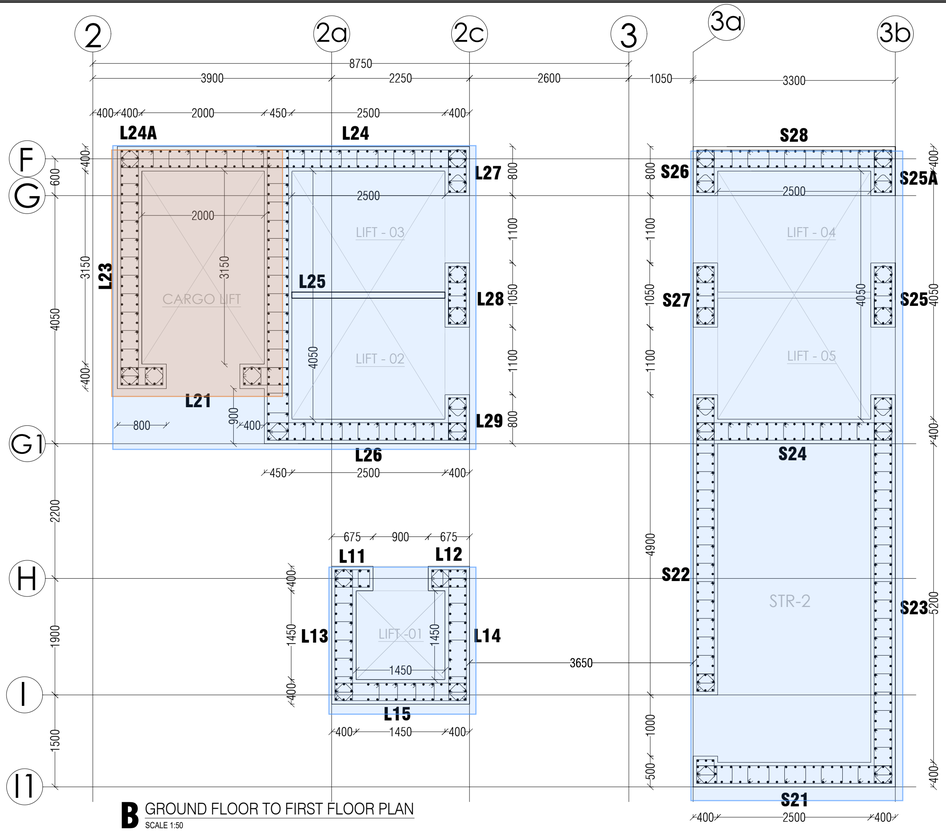


B GROUND FLOOR TO FIRST FLOOR PLAN
SCALE 1:50


NOTE: Contractor to take approval of the consultant for the workshop drawings of Columns & Walls reinforcement details, prepared in accordance to section 18.10 of ACT 318-19 before execution of works.

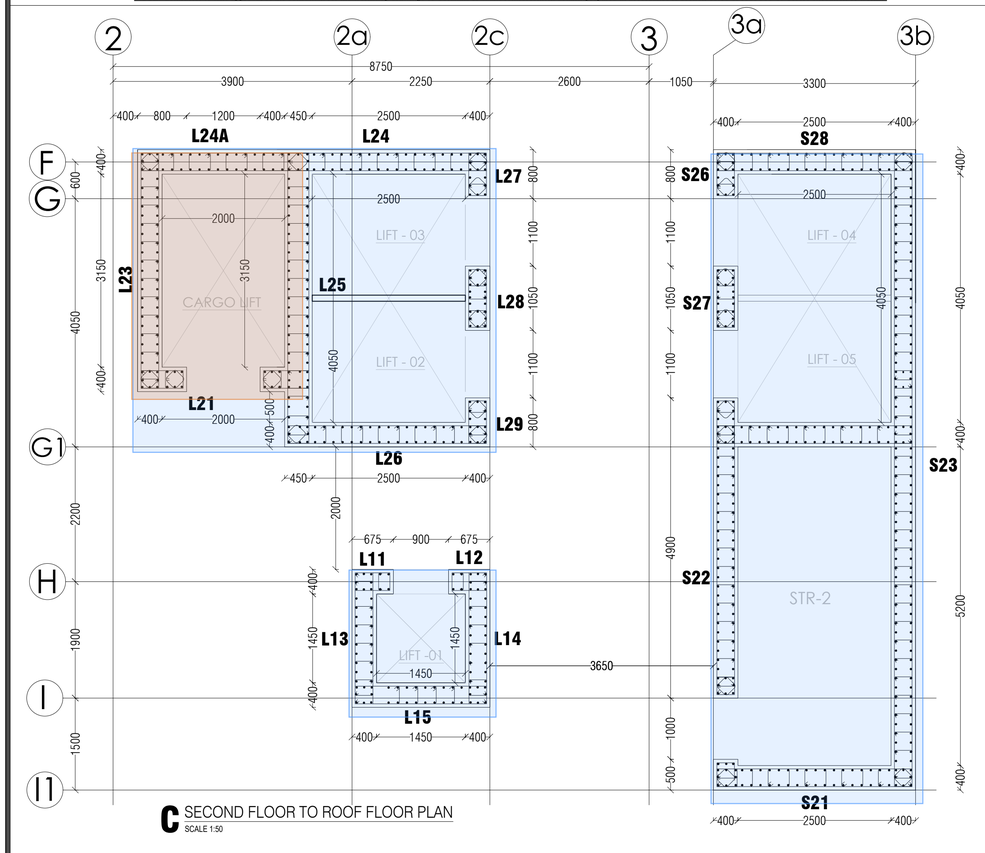

C SECOND FLOOR TO ROOF FLOOR PLAN
SCALE 1:50

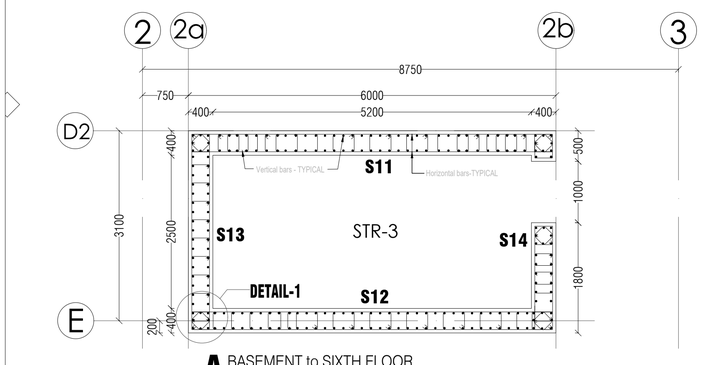


A BASEMENT to SIXTH FLOOR
SCALE 1:50

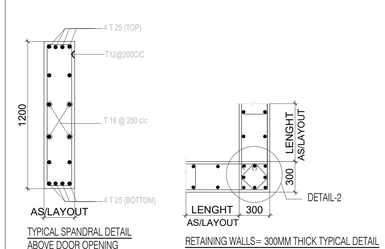

TYPICAL SPANDRAL DETAIL ABOVE DOOR OPENING

RETAINING WALLS= 300MM THICK TYPICAL DETAIL

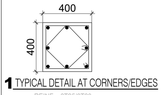

1 TYPICAL DETAIL AT CORNERS/EDGES
REINF. : 8T25/8T20
: T10@150 C/C - TYP.



2 TYPICAL CORNER DETAIL
REINF. : 8T20/8T16
: T10@200 C/C - TYP.

TYPICAL CORNER DETAILS FOR RETAINING WALL

SCHEDULE OF SHEAR WALLS

WALL = S11, S12, S13, S14 = 400MM THK.
2-T25@150c/c-(V) = RAFT TO 3RD FLOOR
2L-T10@125c/c-(H) = RAFT TO 3RD FLOOR
2-T20@150c/c-(V) = 4TH FLOOR TO ROOF
2L-T10@150c/c-(H) = 4TH FLOOR TO ROOF
Boundary Zone for S11 & S12: 1.6m from left and right ends, for S13 & S14: 1.0m from left and right ends.

WALL = S25(GF Only) & S26 - 400MM THK.
2-T32@100c/c-(V) = RAFT TO ROOF
2L-T12@100c/c-(H) = RAFT TO ROOF
Boundary Zone length: 0.5m from left and right ends.

WALL = S27 - 400MM THK.
2-T32@150c/c-(V) = RAFT TO ROOF
2L-T12@100c/c-(H) = RAFT TO ROOF
Boundary Zone length: 0.5m from left and right ends.

WALL = S21 & S28 - 400MM THK.
2-T25@150c/c-(V) = RAFT TO 1ST FLOOR
2L-T12@150c/c-(H) = RAFT TO 1ST FLOOR
2-T20@150c/c-(V) = 2ND FLOOR TO ROOF
2L-T12@150c/c-(H) = 2ND FLOOR TO ROOF
Boundary Zone: 1.3m from left and right ends upto 3rd floor then 0.6m upto roof floor.

WALL = S22,S23 & S24 - 400MM THK.
2-T20@150c/c-(V) = RAFT TO ROOF
2L-T12@125c/c-(H) = RAFT TO ROOF
Boundary Zone: 1.5m from left and right ends upto 3rd floor then 0.6m upto roof floor.

WALL = S25A(GF Only)- 400MM THK.
2-T32@ 70 c/c-(V), T12@125 c/c(H) & Ties.

WALL = L21- 400MM THK.
2-T32@150c/c-(V) = RAFT TO 1ST FLOOR
2L-T12@150c/c-(H) = RAFT TO 1ST FLOOR
2-T25@150c/c-(V) = 2ND FLOOR TO 3RD FLOOR
2L-T12@150c/c-(H) = 2ND FLOOR TO 3RD FLOOR
2-T20@150c/c-(V) = 4TH FLOOR TO ROOF
2L-T10@150c/c-(H) = 4TH FLOOR TO ROOF
Boundary Zone: 0.75m from left and right ends upto roof floor.

WALL = L23 ,L24A , L24 , L25 , L26 - 400MM THK.
2-T25@150c/c-(V) = RAFT TO 1ST FLOOR
2L-T10@150c/c-(H) = RAFT TO 1ST FLOOR
2-T20@150c/c-(V) = 2ND FLOOR TO ROOF
2L-T10@150c/c-(H) = 2ND FLOOR TO ROOF
Boundary Zone for L23 & L24+L24A: 1.4m from left and right ends, for others: 0.9m from left and right ends.

WALL = L27 , L29- 400MM THK.
2-T32@150c/c-(V) = RAFT TO 1ST FLOOR
2L-T12@125c/c-(H) = RAFT TO 1ST FLOOR
2-T25@150c/c-(V) = 2ND FLOOR TO ROOF
2L-T12@150c/c-(H) = 2ND FLOOR TO ROOF
Boundary Zone length: 0.5m from left and right ends.

WALL = L28 - 400MM THK.
2-T25@150c/c-(V) = RAFT TO 1ST FLOOR
2L-T12@150c/c-(H) = RAFT TO 1ST FLOOR
2-T20@150c/c-(V) = 2ND FLOOR TO ROOF
2L-T10@120c/c-(H) = 2ND FLOOR TO ROOF
Boundary Zone length: 0.5m from left and right ends.

WALL = L11 , L12 - 400MM THK.
2-T25@150c/c-(V) = RAFT TO ROOF
2L-T10@150c/c-(H) = RAFT TO ROOF
Boundary Zone length: Full length.

WALL = L13 , L14 , L15 - 400MM THK.
2-T20@150c/c-(V) = RAFT TO ROOF
2L-T10@150c/c-(H) = RAFT TO ROOF
Boundary Zone length: 0.6m from left and right ends.

NOTE: 1) T10@300c/c-HOOK - TYPICAL FOR ALL WALLS
2) In boundary zone lengths at ends of walls all vertical wall reinforcement bars are to be tied with T10 bars as guided by section 18-10 of ACI 318-19.
Consultants prior approval be obtained by the contractor of their workshop drawings before execution of works.

NOTE :

(1) THIS DRAWING IS THE PROPERTY OF :
AL SARAYA ENGINEERING CONSULTANT
P.O.BOX: 49162, DUBAI, U.A.E.
IT IS NOT ALLOWED TO REPRODUCE ITS CONTENTS IN ANY FORM EXCEPT FOR THE PURPOSE FOR WHICH IT IS INTENDED.

(2) THIS DRAWING IS NOT TO BE SCALED. STATED DIMENSIONS ONLY ARE TO BE CONSIDERED. DIMENSIONS ARE IN CENTIMETERS ONLY.

(3) ANY DISCREPANCIES ARE TO BE BROUGHT TO THE ATTENTION OF THE ENGINEER AND RESOLVED BEFORE COMMENCEMENT OF ANY WORK.

NOTES:
1. fcu = 50 N/mm²
2. fy = 460 N/mm²

* ALL THE SERVICE OPENINGS TO BE COORDINATED WITH ARCHITRCTURAL AND MEP DRAWINGS.

NOTE: 34% OPC + 66% GGBS + 5% MICRO SILICA

LEGEND:
- COLUMN CONTINUED TO TOP FLOOR
- COLUMN ENDING AT FLOOR LEVEL
- FLOATING COLUMN STARTING FROM FLOOR LEVEL

CIVIL ENGINEERING DEPARTMENT
Drawing has been reviewed for compliance with the Regulations and is:
NO OBJECTION
Permit Engineer: ..... Date .....

Subject to compliance with designed codes, approved architectural and structural, EHS regulation and Dubai civil defence requirments

AL SARAYA ENGINEERING CONSULTANTS
السرايا للاستشارات الهندسية
P.O.Box 49162 Tel.: 04-3350084
Dubai - U.A.E. Fax: 04-3350087

REVISIONS:

NO.	DESCRIPTION:	DATE:
00	FOR TENDER	---
01	FOR APPROVAL	13.01.25
02	FOR BP APPROVAL	24.04.25
03	FOR BP APPROVAL	16.06.25
04		

DEVELOPER:
B M L INVESTMENT LLC

OWNER:
DUBAI ISLANDS L.L.C

DESIGNER:

CONSULTANT:
AL SARAYA ENGINEERING CONSULTANTS
السرايا للاستشارات الهندسية
Architects , Engineers , Planners P.O.Box - 49162 , DUBAI, U.A.E.
Tel 04-3350084 Fax 04-3350087 E-mail :sarayadx@emirates.net.ae

SUSTAINABLE & MEP CONSULTANT
CONSISTENT ENGINEERING CONSULTANTS
Post Box No: 125786, Office 2001 & 2002, API World Tower, Sheikh Zayed Road, Opp. World Trade Centre, Dubai.
Tel: +971-4 3860601
Fax: +971-4 3860602
Email: info@consistentconsultants.com
Website: consistentconsultants.com

COMMUNITY: NAKHLAT DEIRA-101 PLOT: 1010619

PROJECT:
PROPOSED B+G+7+R HOTEL
ON PLOT NO.DIA-WE-0032(1010619),
NAKHLAT DEIRA-101,DUBAI

DRG. TITLE:
SHEAR WALL DETAILS

SCALE:	1:150/A1	KEY:	–
APPROVED BY:	SJ	DRAWN BY:	SPP
DATE:	--	PLOTTED ON:	–
PRELIMINARY	FINAL	ADDITION	REVISION
ISSUED FOR:	—		

JOB NO. : 624

DRG. NO.: S-110

REV. 00